



PORTFOLIO ASHLYN BROWN

01

KUFTA RESIDENCE

Organic Forms
Showy Flowers

02

STEWART RESIDENCE

Natural Screening
BBQ Patio

03

MAYHEW RESIDENCE



Forest Terrace
Shaded Gardens

04

OLD MNT ROAD

Robust
Curb Appeal


TABLE OF CONTENTS

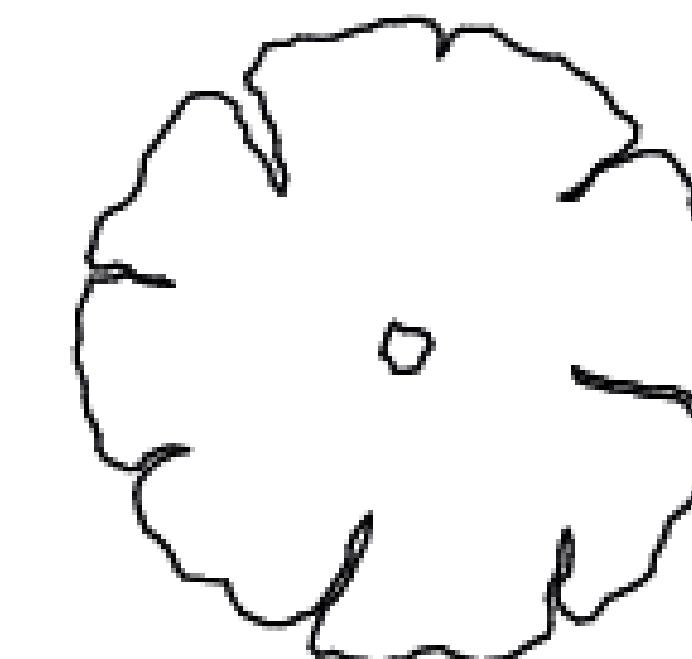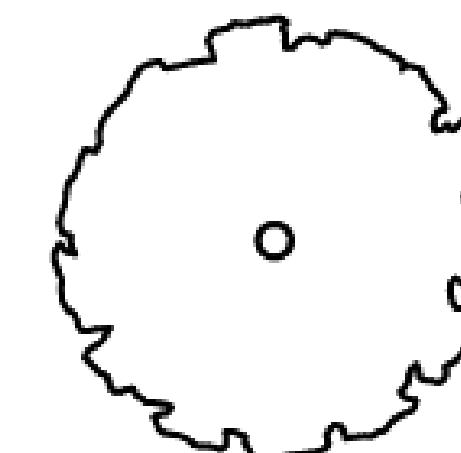

KUFTA RESIDENCE

CHARLOTTESVILLE


A thoughtfully curated, budget-conscious landscape design emphasizing organic forms and vibrant color. Featuring lush flowering plants anchored by ornamental trees for year-round interest.

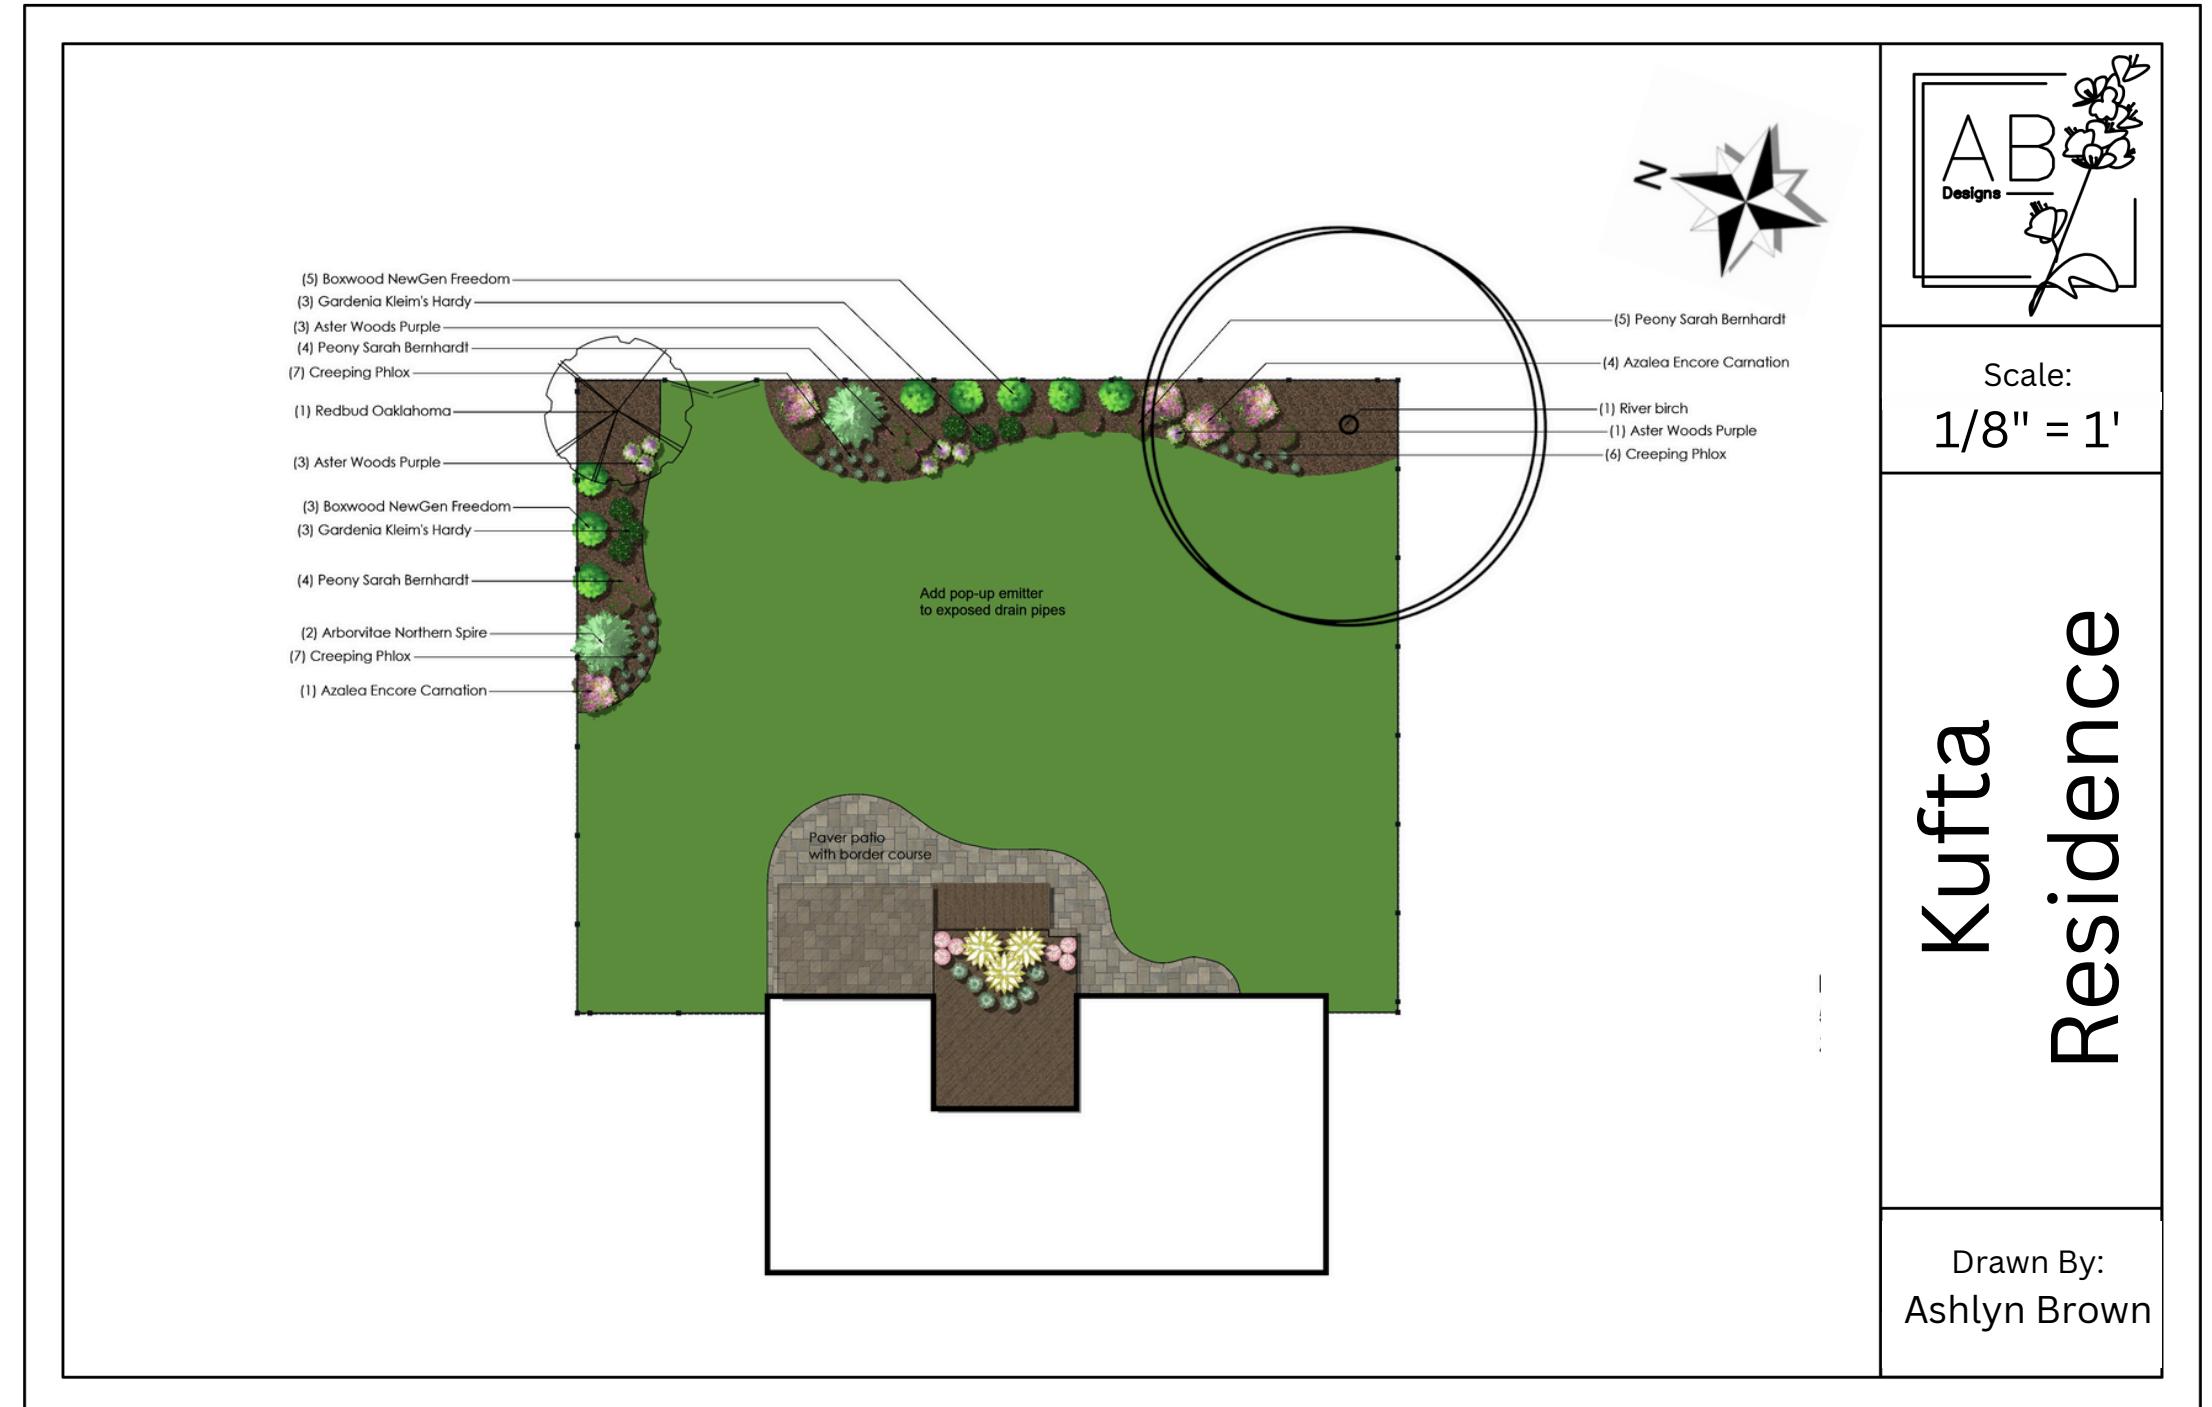

STEWART RESIDENCE

CHARLOTTESVILLE


A privacy focused landscape featuring dense evergreen screening for year-round seclusion, including coverage for a tucked away hot tub retreat. The design also incorporates a functional and inviting BBQ patio.

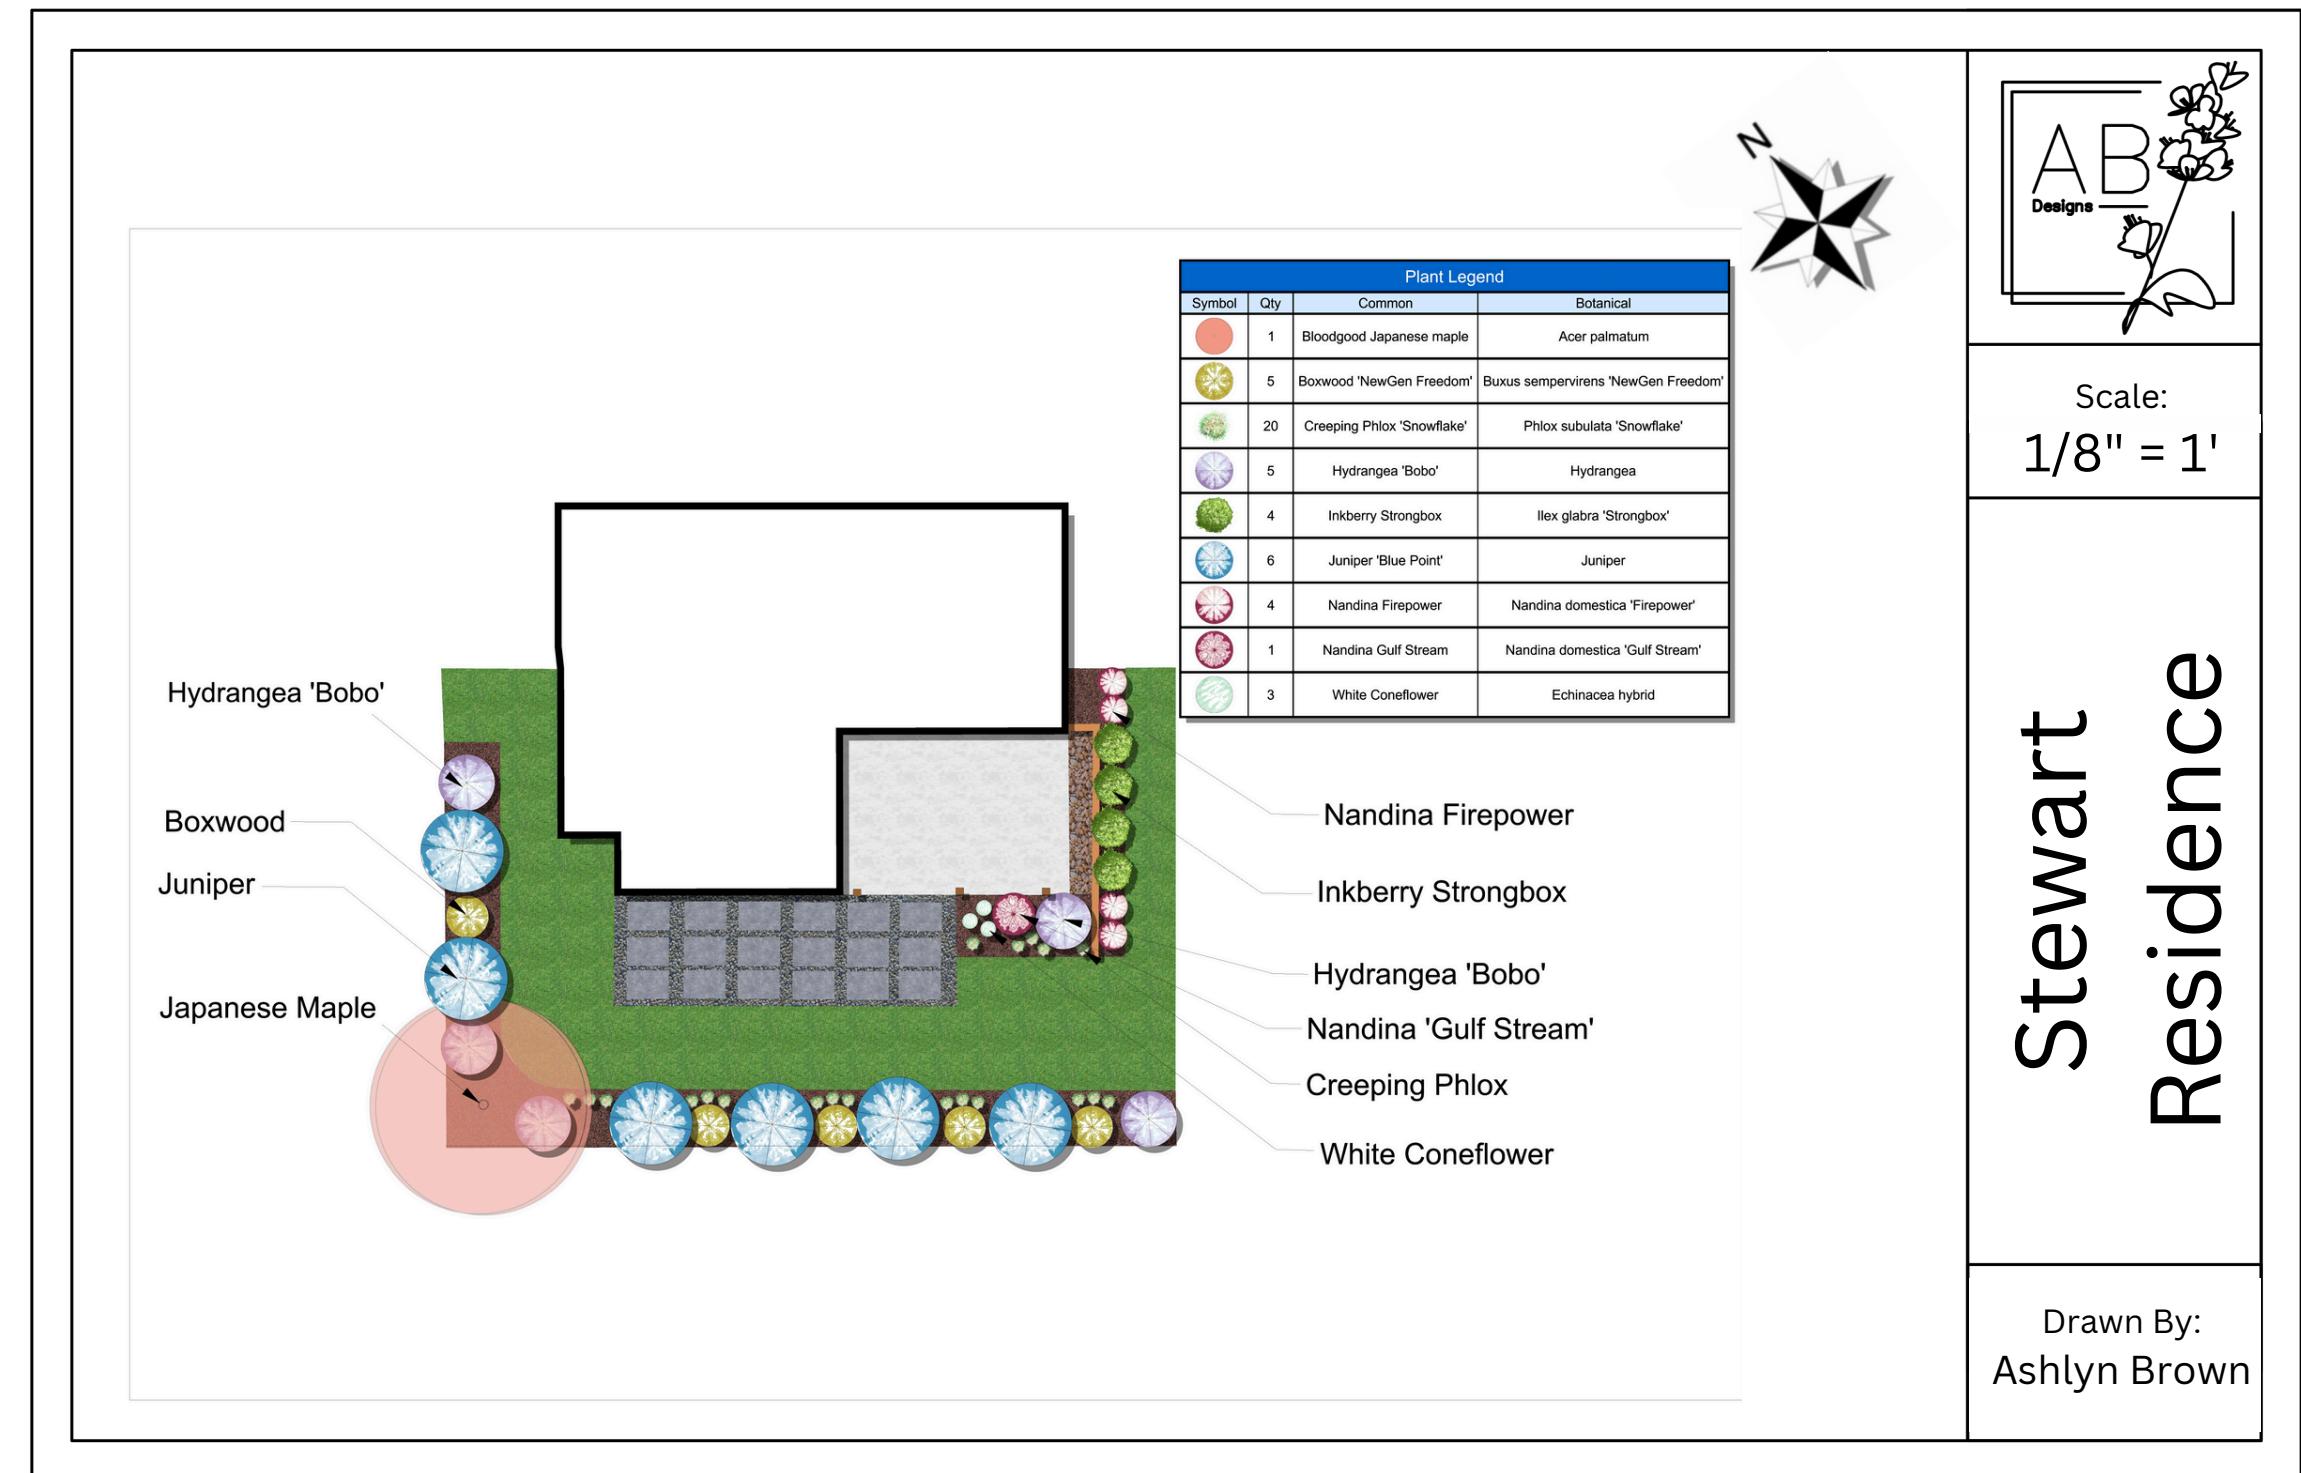

MAYHEW RESIDENCE

PALMYRA

This design embraces a shaded woodland aesthetic. Evergreen shrubs anchor the entryway, surrounded by a natural forest landscape. The terraced side yard features flowing plantings that guide the eye toward the serene lake beyond.

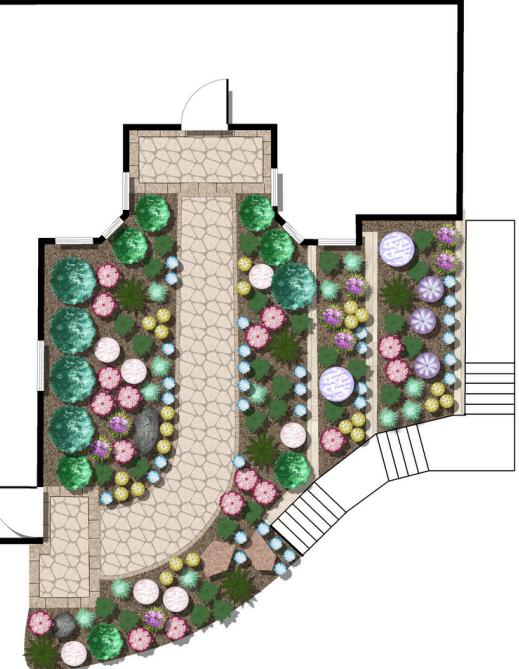

Scale:
1" = 10'

Mayhew
Residence


Drawn By:
Ashlyn Brown

Plant Legend			
Symbol	Qty	Common	Botanical
	2	Agastache	<i>Agastache foeniculum</i>
	3	Allium 'Medusa'	<i>Allium</i>
	7	Astilbe 'Gloria Purpurea'	<i>Astilbe</i>
	29	Autumn Fern	<i>Dryopteris erythrosora</i>
	8	Bleeding Heart 'Eximia'	<i>Dicentra eximia</i>
	5	Boxwood 'Dee Runk'	<i>Buxus sempervirens</i>
	23	Dwarf Crested Iris	<i>Iris cristata</i>
	12	Foam Flower	<i>Tiarella</i>
	17	Hellebore 'Ice n Roses Rose'	<i>Helleborus hybrid</i>
	6	Holly Fern	<i>Cyrtomium falcatum 'Rochfordianum'</i>
	7	NewGen Independence	<i>Buxus 'NewGen Independence'</i>
	33	Sweet Woodruff	<i>Galium odoratum</i>

OLD MTN ROAD

LOUISA, VA

A simple yet impactful design intended to boost curb appeal for a trailer home. Bright, bold plantings add create a welcoming and vibrant first impression.

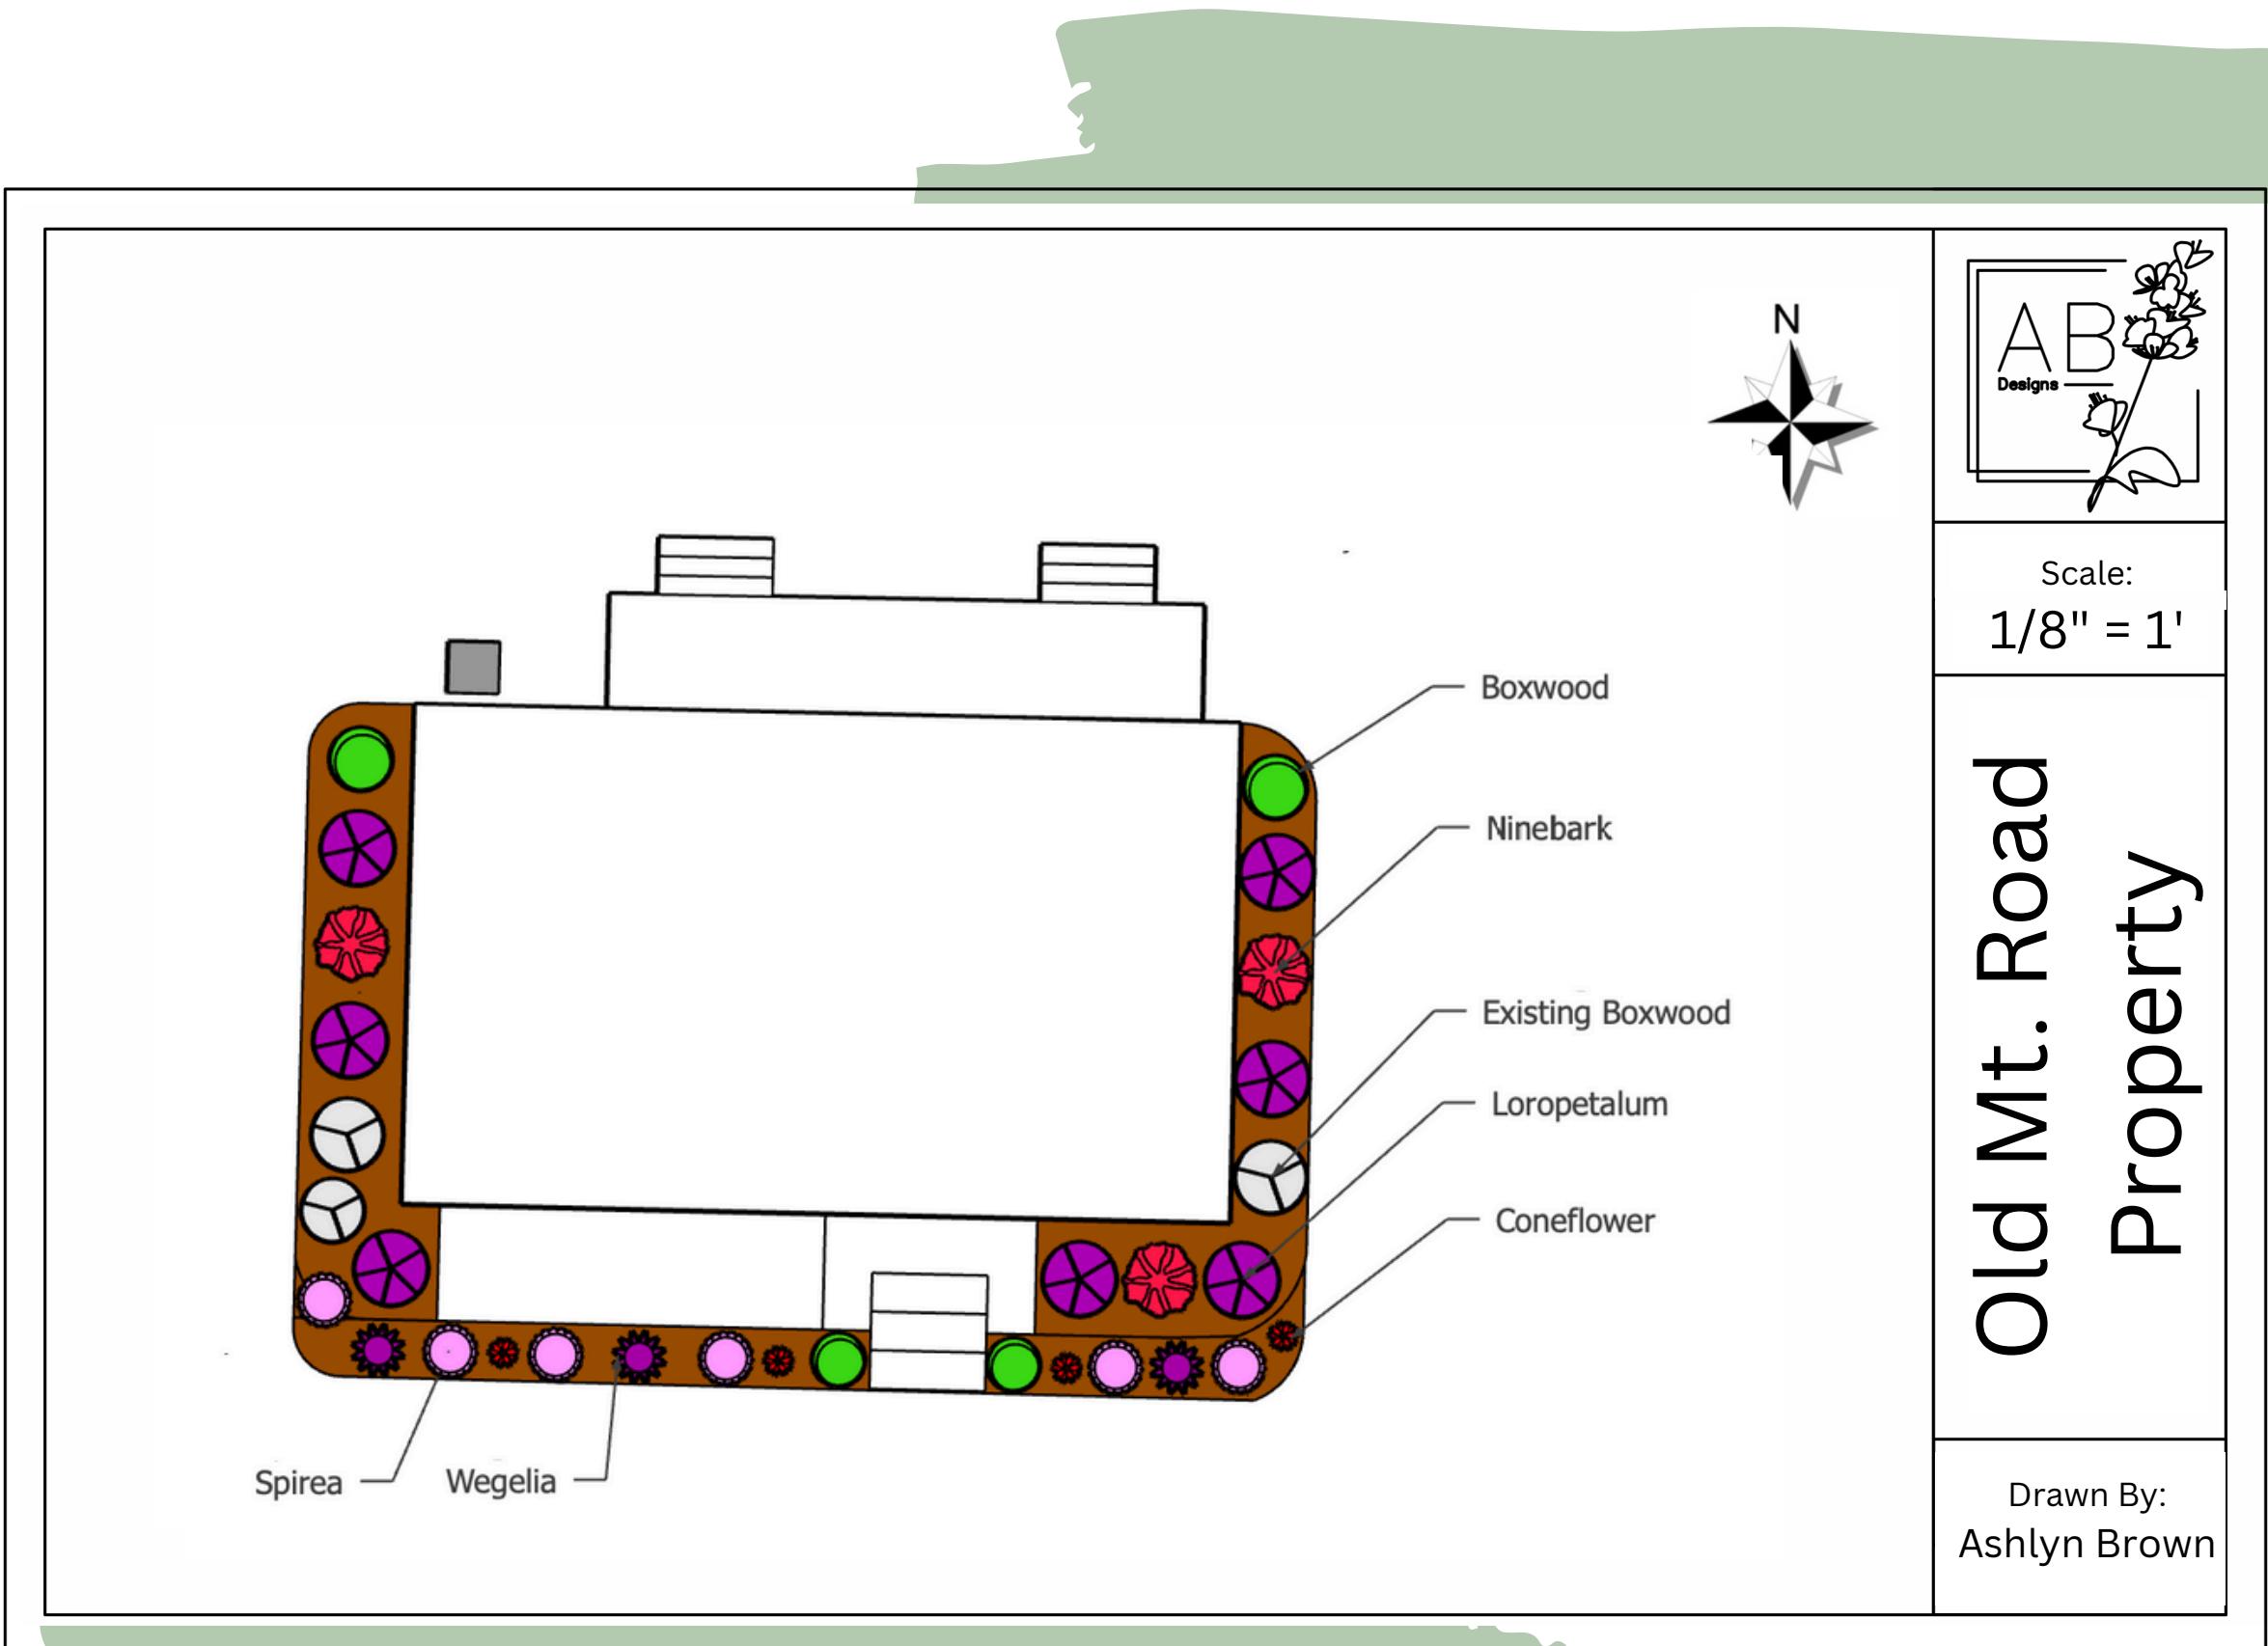



ASHLYN BROWN

801-707-7461

its.ashlynrae@gmail.com

